

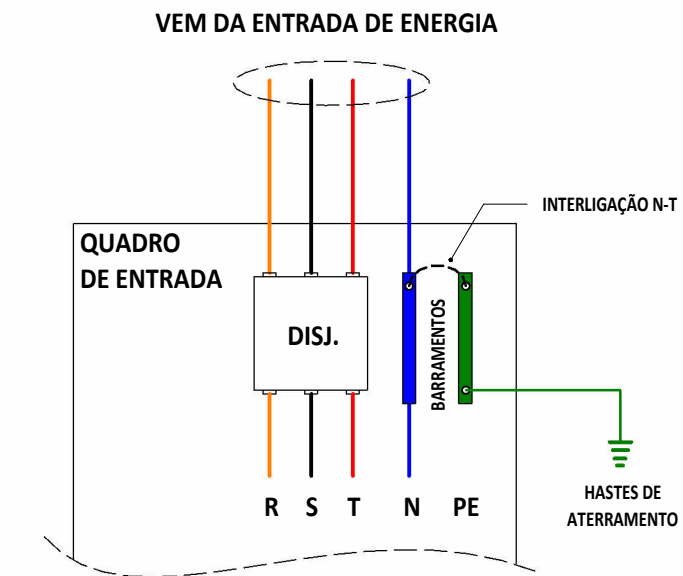
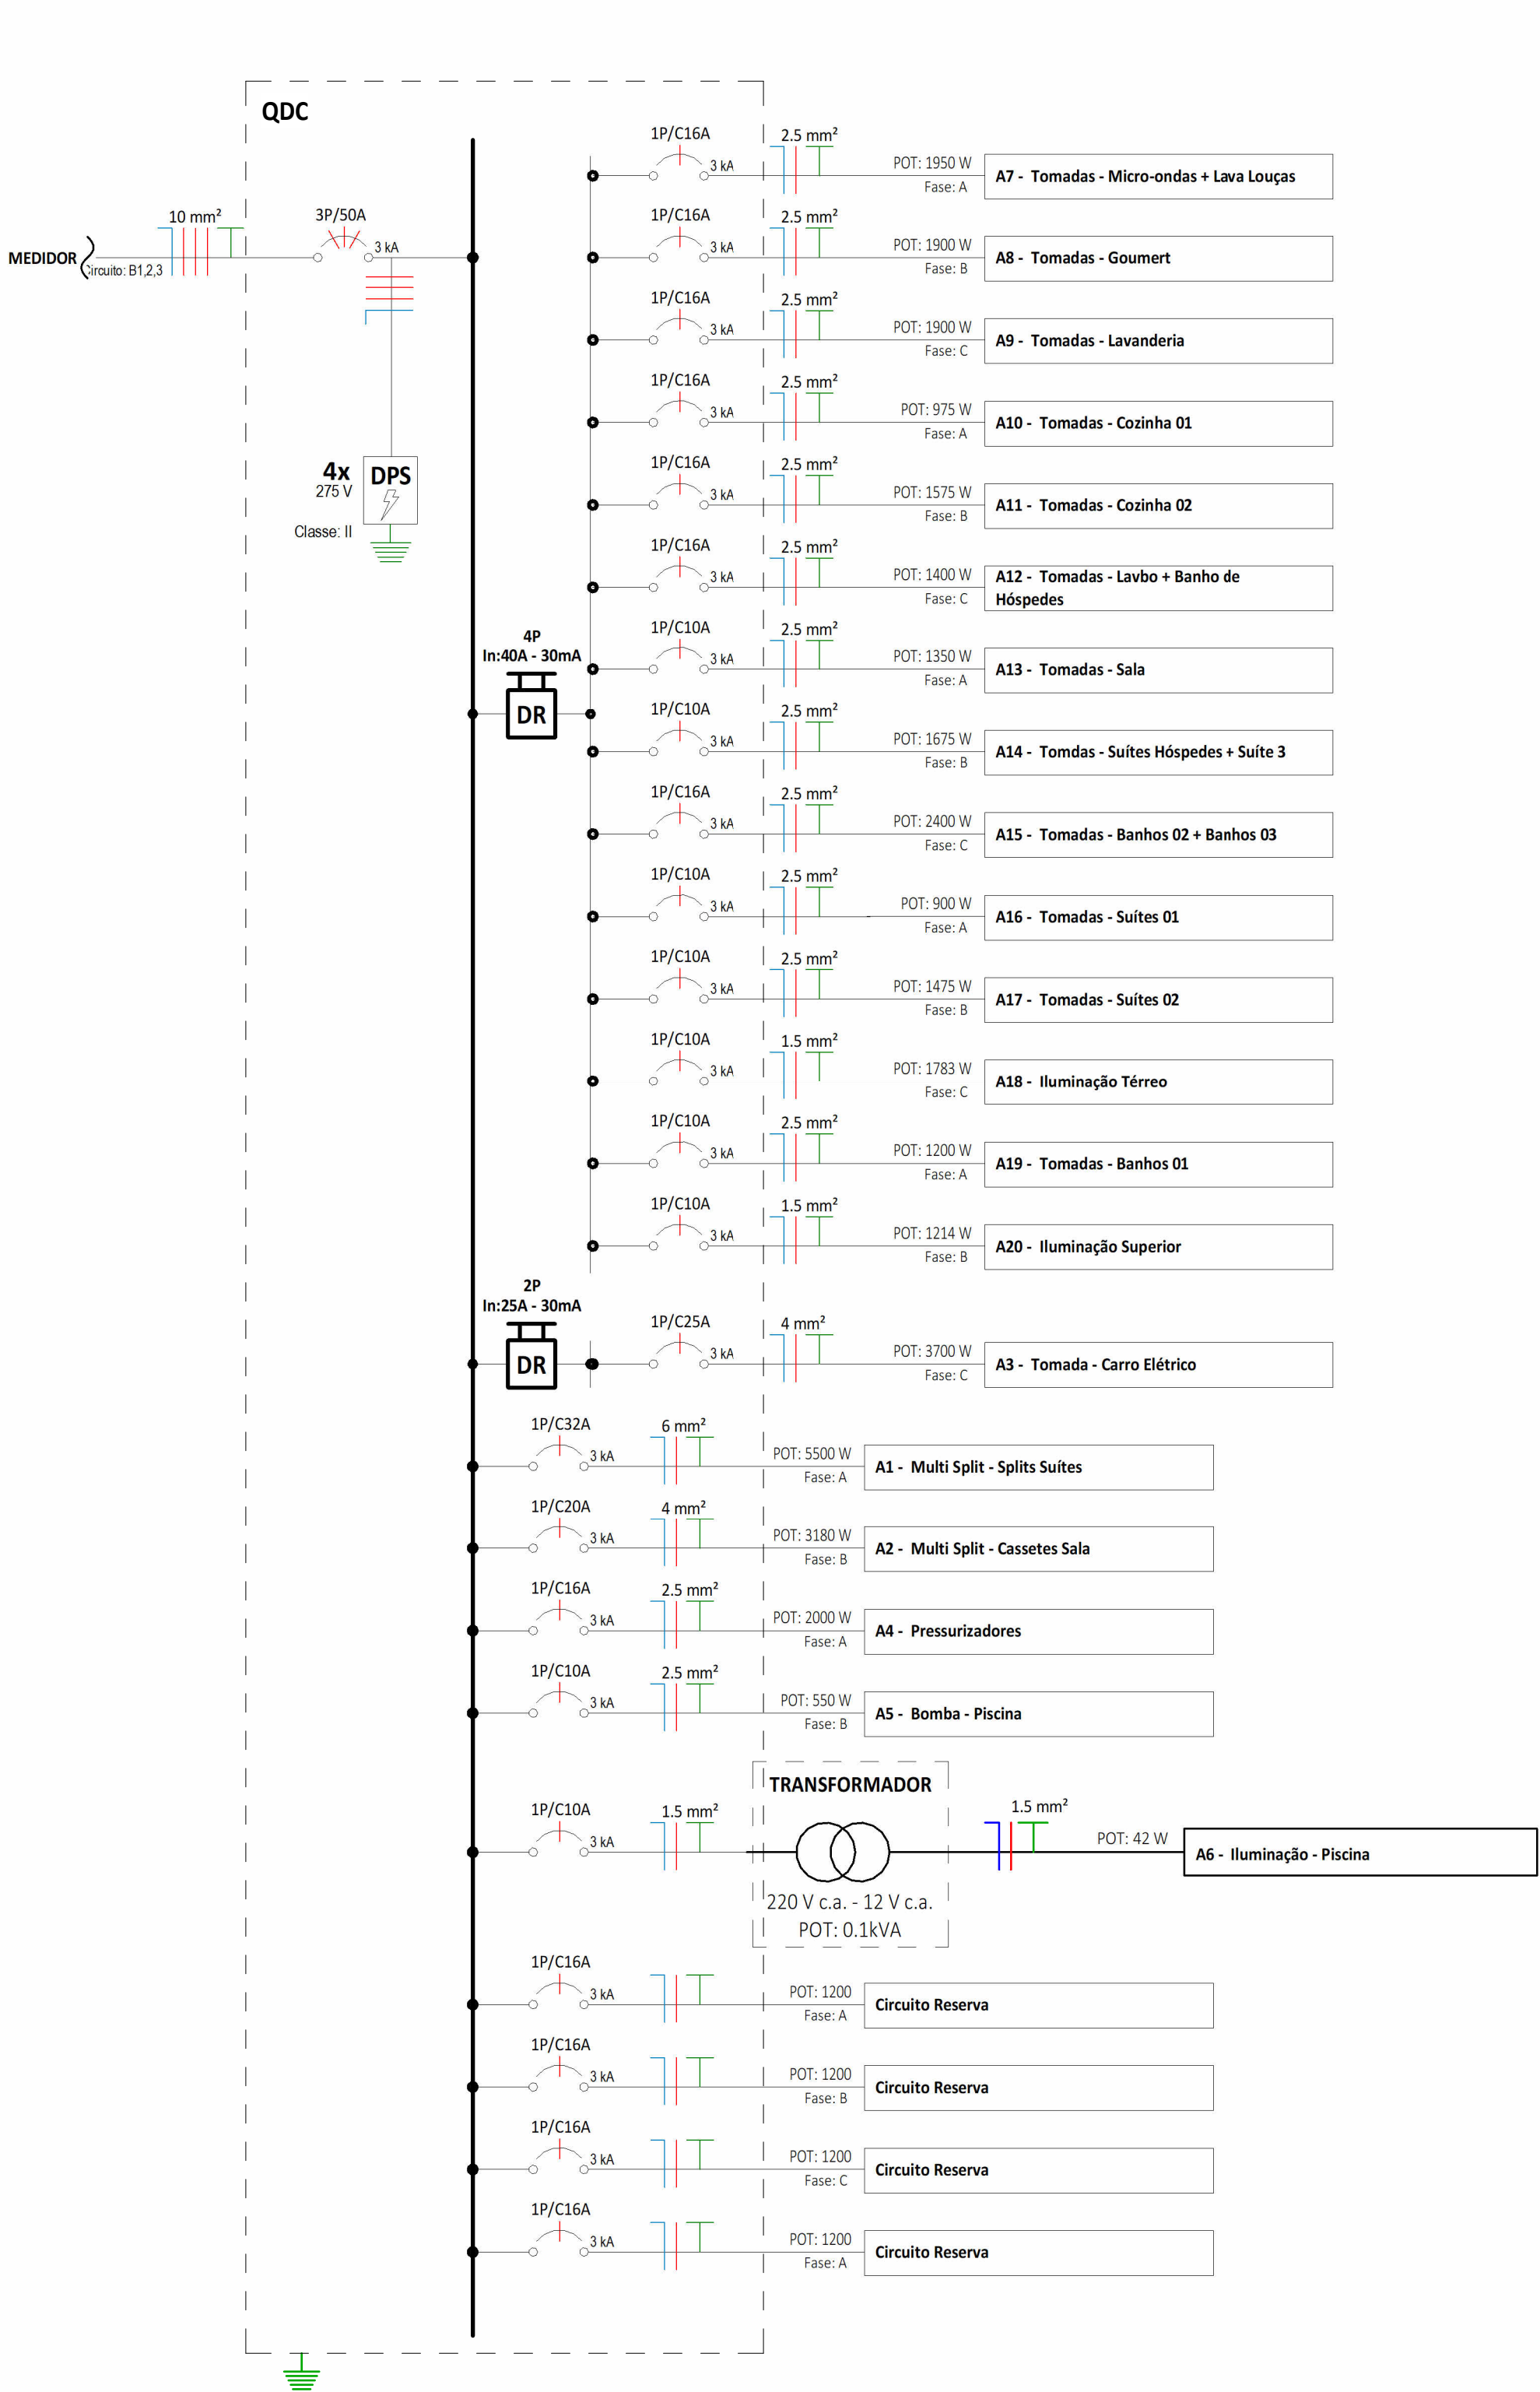


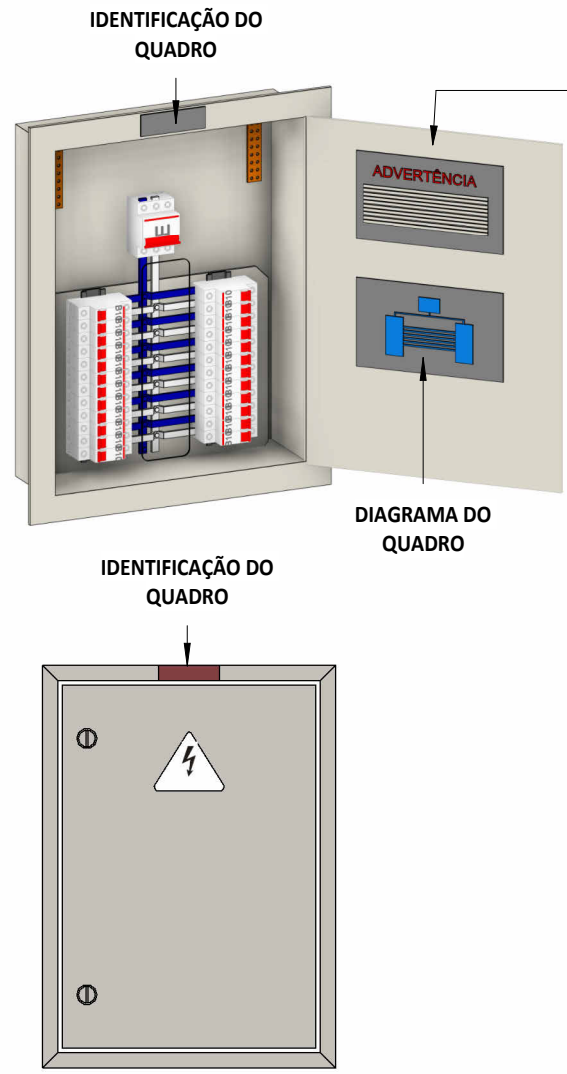

3 ESQUEMA DE ATERRAMENTO TIPO TN-S

S/ ESCALA

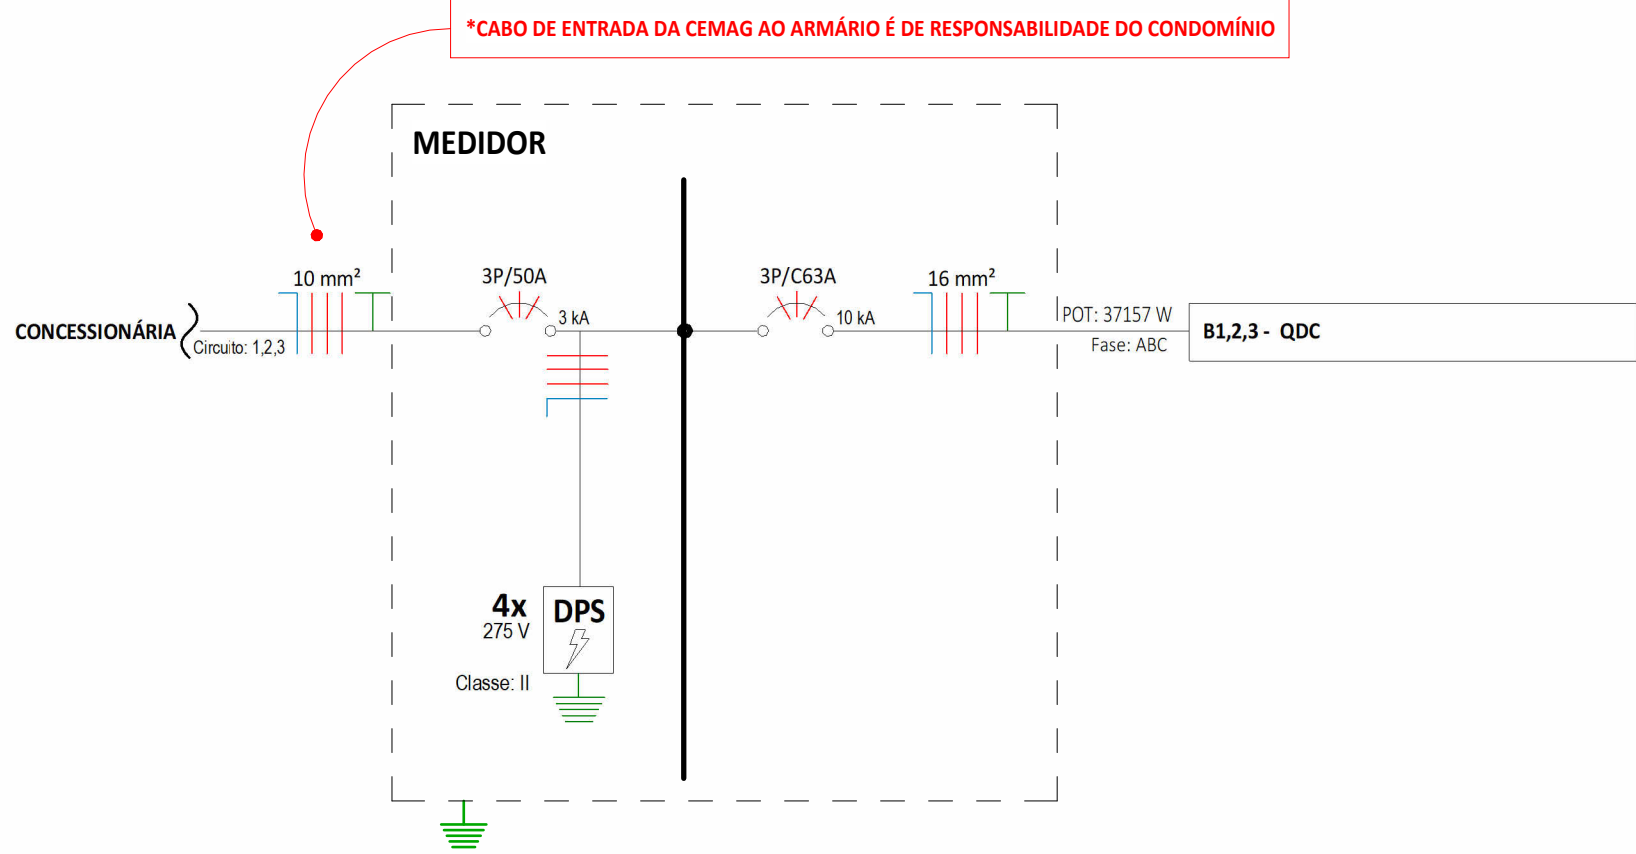

ADVERTÊNCIA

1-Quando um disjuntor ou fusível atua, desligando algum circuito ou a instalação inteira, a causa pode ser uma sobrecarga ou um curto-circuito. Desligamentos frequentes são sinal de sobrecarga. Por isso, NUNCA troque seus disjuntores ou fusíveis por outros de maior corrente (maior amperagem), simplesmente. Como regra, a troca de um disjuntor ou fusível por outro de maior corrente requer, antes, a troca dos fios e cabos elétricos, por outros de maior seção (bitola).

2-Da mesma forma, NUNCA desative ou remova a chave automática de proteção contra choques elétricos (dispositivo DR), mesmo em caso de desligamentos sem causa aparente. Se os desligamentos forem frequentes e, principalmente, se as tentativas de religar a chave não tiverem êxito, isso significa, muito provavelmente, que a instalação elétrica apresenta anomalias internas, que só podem ser identificadas e corrigidas por profissionais qualificados. A DESATIVAÇÃO OU REMOÇÃO DA CHAVE SIGNIFICA A ELIMINAÇÃO DE MEDIDA PROTETORA CONTRA CHOQUES ELÉTRICOS E RISCO DE VIDA PARA OS USUÁRIOS DA INSTALAÇÃO.

2 INSTALAÇÃO PADRÃO DE QUADROS ELÉTRICOS

S/ ESCALA

QUADRO DE CARGAS QDC													
Circuito	Descrição	Tensão	Potência Ativa	Fator de Potência	Corrente	Disjuntor	Isolação do Cabo	Condutor por Fase	Seção do Condutor (mm²)	Queda de Tensão	Fase R	Fase S	Fase T
QDC													
A1	Multi Split - Splits Suítes	220 V	5500 W	1,00	25,00 A	32,00 A	EPR	1	6	0,77	5500 W		
A2	Multi Split - Cassetes Sala	220 V	3180 W	1,00	14,45 A	20,00 A	EPR	1	4	0,68		3180 W	
A3	Tomada - Carro Elétrico	220 V	3700 W	1,00	16,82 A	25,00 A	EPR	1	4	0,86			3700 W
A4	Pressurizadores	220 V	2000 W	1,00	9,09 A	16,00 A	EPR	1	2,5	0,89	2000 W		
A5	Bomba - Piscina	220 V	550 W	1,00	2,50 A	10,00 A	PVC	1	2,5	0,35		550 W	
A6	Iluminação - Piscina	220 V	41,84 W	1,00	0,19 A	10,00 A	PVC	1	1,5	0,05			41,84 W
A7	Tomadas - Micro-ondas + Lava Louças	220 V	1950 W	1,00	8,86 A	16,00 A	PVC	1	2,5	0,25	1950 W		
A8	Tomadas - Goumert	220 V	1900 W	1,00	8,64 A	16,00 A	PVC	1	2,5	0,77		1900 W	
A9	Tomadas - Lavanderia	220 V	1900 W	1,00	8,64 A	16,00 A	PVC	1	2,5	0,77			1900 W
A10	Tomadas - Cozinha 01	220 V	975 W	1,00	4,44 A	16,00 A	PVC	1	2,5	0,20	975 W		
A11	Tomadas - Cozinha 02	220 V	1575 W	1,00	7,16 A	16,00 A	PVC	1	2,5	0,77		1575 W	
A12	Tomadas - Lavbo + Banho de Hóspedes	220 V	1400 W	1,00	6,36 A	16,00 A	PVC	1	2,5	0,04			1400 W
A13	Tomadas - Sala	220 V	1350 W	1,00	6,14 A	10,00 A	PVC	1	2,5	0,25	1350 W		
A14	Tomdas - Suítes Hóspedes + Suite 3	220 V	1675 W	1,00	7,62 A	10,00 A	PVC	1	2,5	0,61		1675 W	
A15	Tomadas - Banhos 02 + Banhos 03	220 V	2400 W	1,00	10,91 A	16,00 A	PVC	1	2,5	0,04			2400 W
A16	Tomadas - Suítes 01	220 V	900 W	1,00	4,09 A	10,00 A	PVC	1	2,5	0,48	900 W		
A17	Tomadas - Suítes 02	220 V	1475 W	1,00	6,70 A	10,00 A	PVC	1	2,5	0,58		1475 W	
A18	Iluminação Térreo	220 V	1783,36 W	0,92	8,81 A	10,00 A	PVC	1	1,5	0,53			1783,36 W
A19	Tomadas - Banhos 01	220 V	1200 W	1,00	5,45 A	10,00 A	PVC	1	2,5	0,03	1200 W		
A20	Iluminação Superior	220 V	1214,4 W	0,92	6,00 A	10,00 A	PVC	1	1,5	0,50		1214,4 W	
MEDIDOR													
B1,2,3	QDC	380 V	36669,6 W	1,00	55,76 A	50,00 A	EPR	3	10		13875 W	11569,4 W	11225,2 W

LEGENDA DOS QUADROS		
SIGLA QUADRO	DESCRIÇÃO	PREFIXO
Térreo		
QDC		A



DIAGRAMA E QUADRO DE CARGAS

EXECUTIVO

ELE_CARNAÚBA 153_R00

001

R00